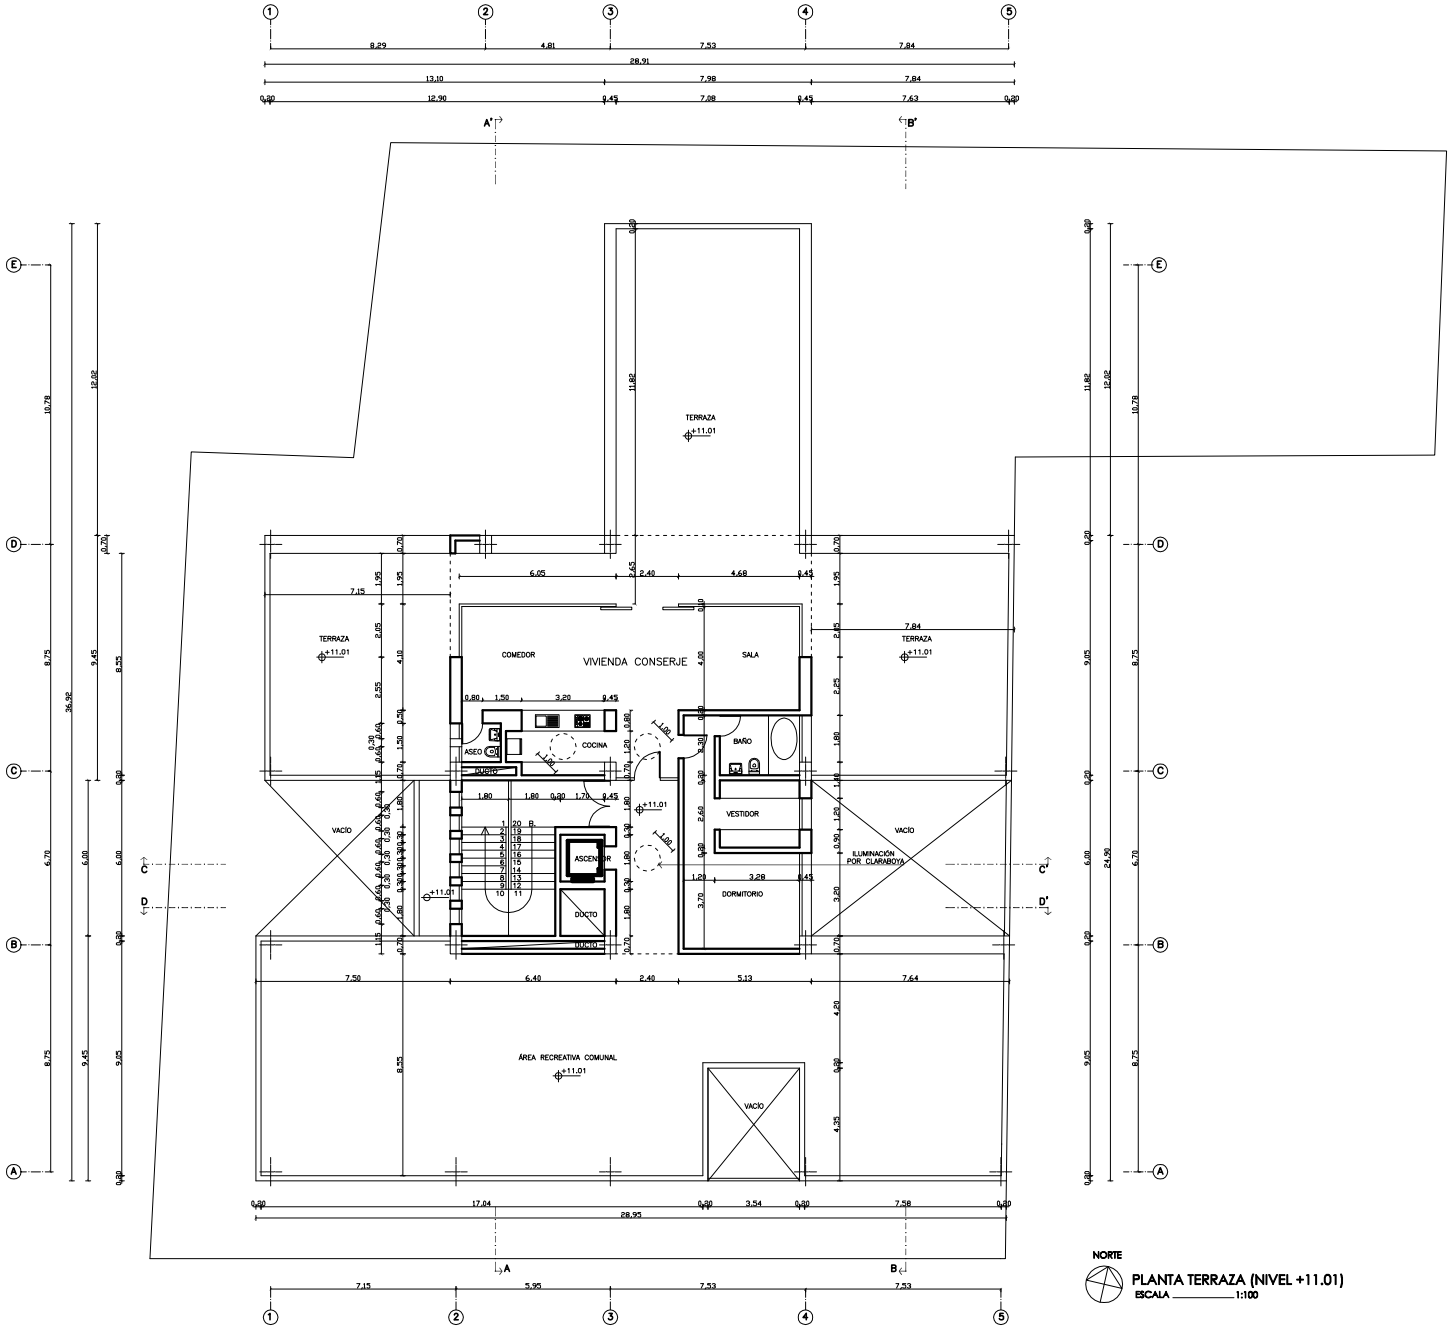

NORTE

PLANTA TERRAZA (NIVEL +11.01)

ESCALA _____ 1:100

PROYECTO ARQUITECTÓNICO
EDIFICIO "REYPAZ"

N. DE PREDIO:	UBICACIÓN: AV. RUMIÑAHUI S1-18 Y ROOSEVELT, LATACUNGA	FECHA: MAYO / 2021
C. CATASTRAL: 050101401051-00040	CONTIENE: PLANTA CUARTA (N.+11.01)	ESCALA: INDICADAS
EQUIPO DE PROYECTO: ARQ. PATRICIO GUERRERO ARQ. VERÓNICA GUERRERO ARQ. DARWIN SÁNCHEZ		LÁMINA: A 6/7
PROPIETARIO: EMPRESA "CONSERPAZ CÍA. LTDA."		PROYECTO ARQUITECTÓNICO:
DOCTOR EMILIO REYES ZAPATA GERENTE "CONSERPAZ" RUC: 0501767979001		ARQ. PATRICIO GUERRERO SEGOVIA C.I. 0502052948 REGISTRO SENESCYT: 1023-05-0561158

OBSERVACIONES:

SELLOS MUNICIPALES: