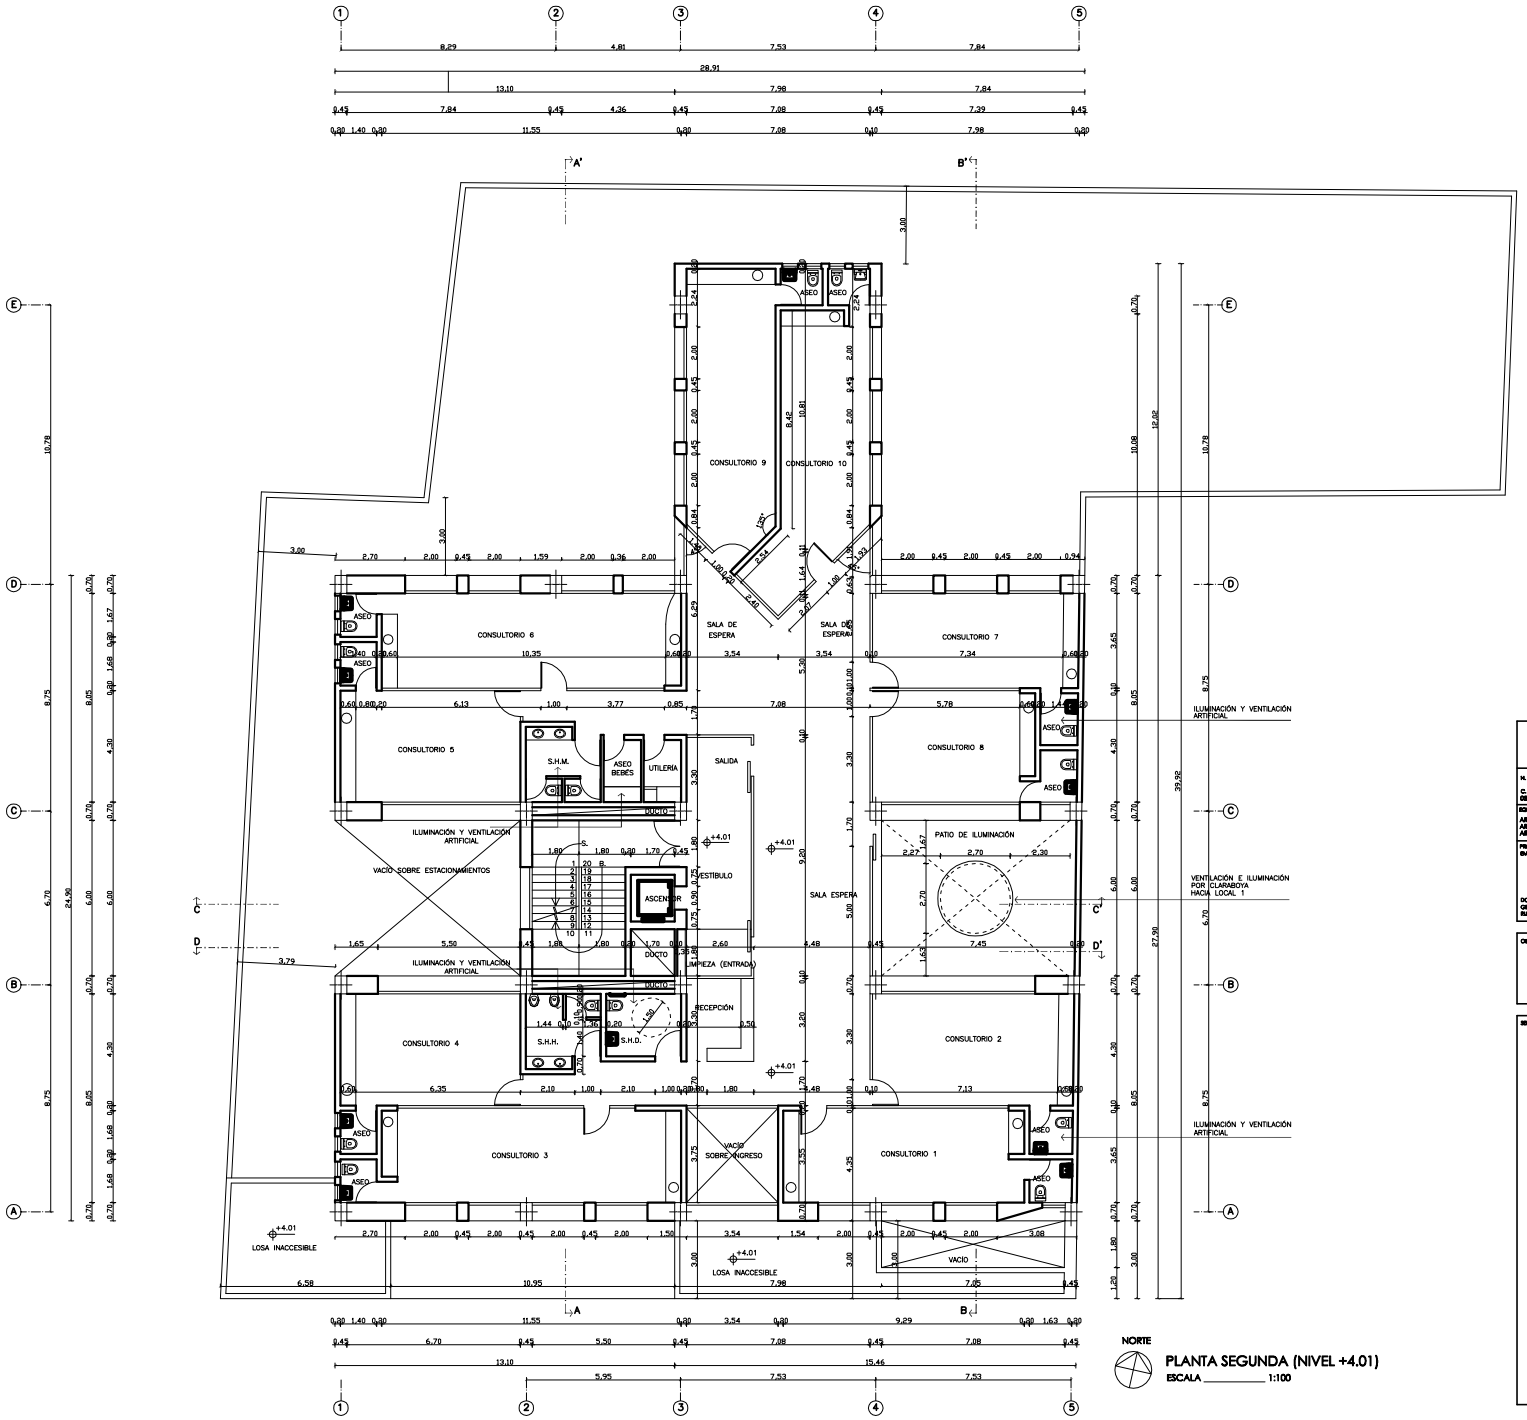

PLANTA SEGUNDA (NIVEL +4.01)

ESCALA _____ 1:100

PROYECTO ARQUITECTÓNICO
EDIFICIO "REYPAZ"

N. DE PREDIO:	UBICACIÓN: AV. RUMIÑAHUI S1-18 Y ROOSEVELT, LATACUNGA	FECHA: MAYO / 2021
C. CATASTRAL: 050101401051-00040	CONTIENE: PLANTA SEGUNDA (N. +4.01)	ESCALA: INDICADAS
EQUIPO DE PROYECTO: ARQ. PATRICIO GUERRERO ARQ. VERÓNICA GUERRERO ARQ. DARWIN SÁNCHEZ		LÁMINA: A 3/9
PROPIETARIO: EMPRESA "CONSTRUPAZ CÍA. LTDA."		PROYECTO ARQUITECTÓNICO:
DOCTOR EMILIO REYES ZAPATA CÉDULA: 1200291448 RUC: 0501767170001		ARQ. PATRICIO GUERRERO SEGOVIA C.I. 0502052448 REGISTRO SENESCYT: 1032-04-0861-08

OBSERVACIONES:

S.H.H.____ SERVICIOS HIGIÉNICOS HOMBRES
S.H.M.____ SERVICIOS HIGIÉNICOS MUJERES
S.H.D.____ SERVICIOS HIGIÉNICOS DISCAPACITADOS

SELLOS MUNICIPALES: